


DETAILS OF GRADES STEEPER THAN 1 IN 1200 UPTO & 1 IN 400 WITHIN YARD LIMITS


Sl. No.	LOCALITIES	NAME OF STRUCTURE WHICH INFRINGE	PRESCRIBED MAXIMUM/ MINIMUM DIMENSIONS CHAPTER II, ITEM NO. 2 OF SCHEDULE OF DIMENSIONS	EXISTING ACTUAL DIMENSIONS	AMOUNT OF INFRINGEMENT	Remarks	
1.	POTHULAPADU YARD	Ch: 227596m (FCSB: 286m) to Ch: 227900m (FCSB: 599m) For Main Line	CHAPTER II, ITEM NO. 2 OF SCHEDULE OF DIMENSIONS	1 in 1200 (0.083%)	1 in 920 (0.108%)	(0.024%)	The existing gradients are provided during gauge conversion. The recommended gradient of 1 in 1200 couldn't be provided for the stretches 1:2.83 as given as it requires lifting of track by 7.29m, 31.4m, 31.57m respectively. As the quantum of lift is significant and it involves lifting of track features in order to comply with SDO, hence, this needs to be avoided as it is not practicable.
2.	POTHULAPADU YARD	Ch: 227900m (FCSB: 599m) to Ch: 228100m (FCSB: 790m) For Main Line	CHAPTER II, ITEM NO. 2 OF SCHEDULE OF DIMENSIONS	1 in 1200 (0.083%)	1 in 415 (0.24%)	(0.157%)	
3.	POTHULAPADU YARD	Ch: 228334m (FCSB: 1024m) to Ch: 228575m (FCSB: 1265m) For Main Line	CHAPTER II, ITEM NO. 2 OF SCHEDULE OF DIMENSIONS	1 in 1200 (0.083%)	1 in 466.67 (0.214%)	(0.131%)	

S.No	Between stations	Kilometre	Restriction in kmph	Direction	Reason
1	MOA-PUPU	218/16-220/1	75	DOWN	Consolidation of Track
2	MOA-PUPU	220/4-17	100	DOWN	2.5 Degree Curve No.93
3	PUPU-ALPR	230/13-230/14	90	DOWN	Low Height of RUB and Tram Way OHE
4	PUPU-ALPR	232/10-236/13	75P/50G	DOWN	Yielding Formation
5	ALPR-PUPU	236/13-232/10	75P/50G	UP	Yielding Formation
6	ALPR-PUPU	230/14-230/13	90	UP	Low Height of RUB and Tram Way OHE
7	PUPU-MOA	220/17-220/4	100	UP	2.5 Degree Curve No.93
8	PUPU-MOA	220/1-218/16	75	UP	Consolidation of Track

228 KM

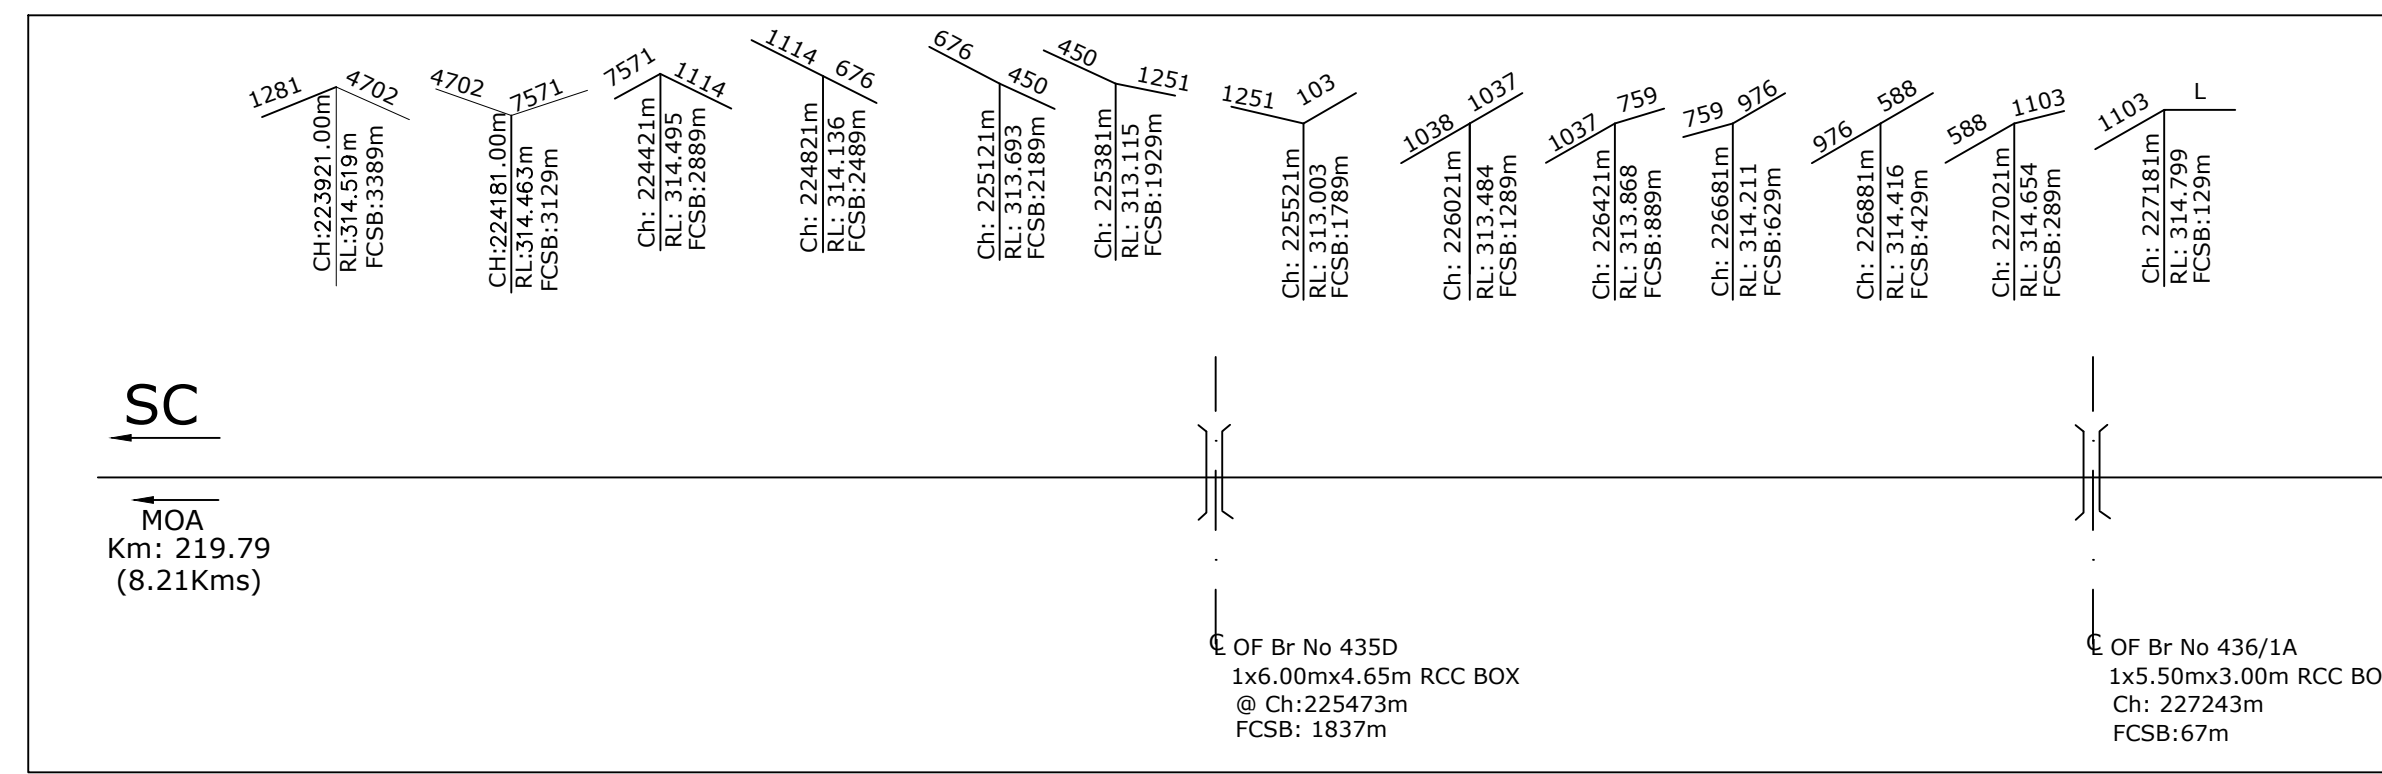

3 Km DETAILS ON SC END

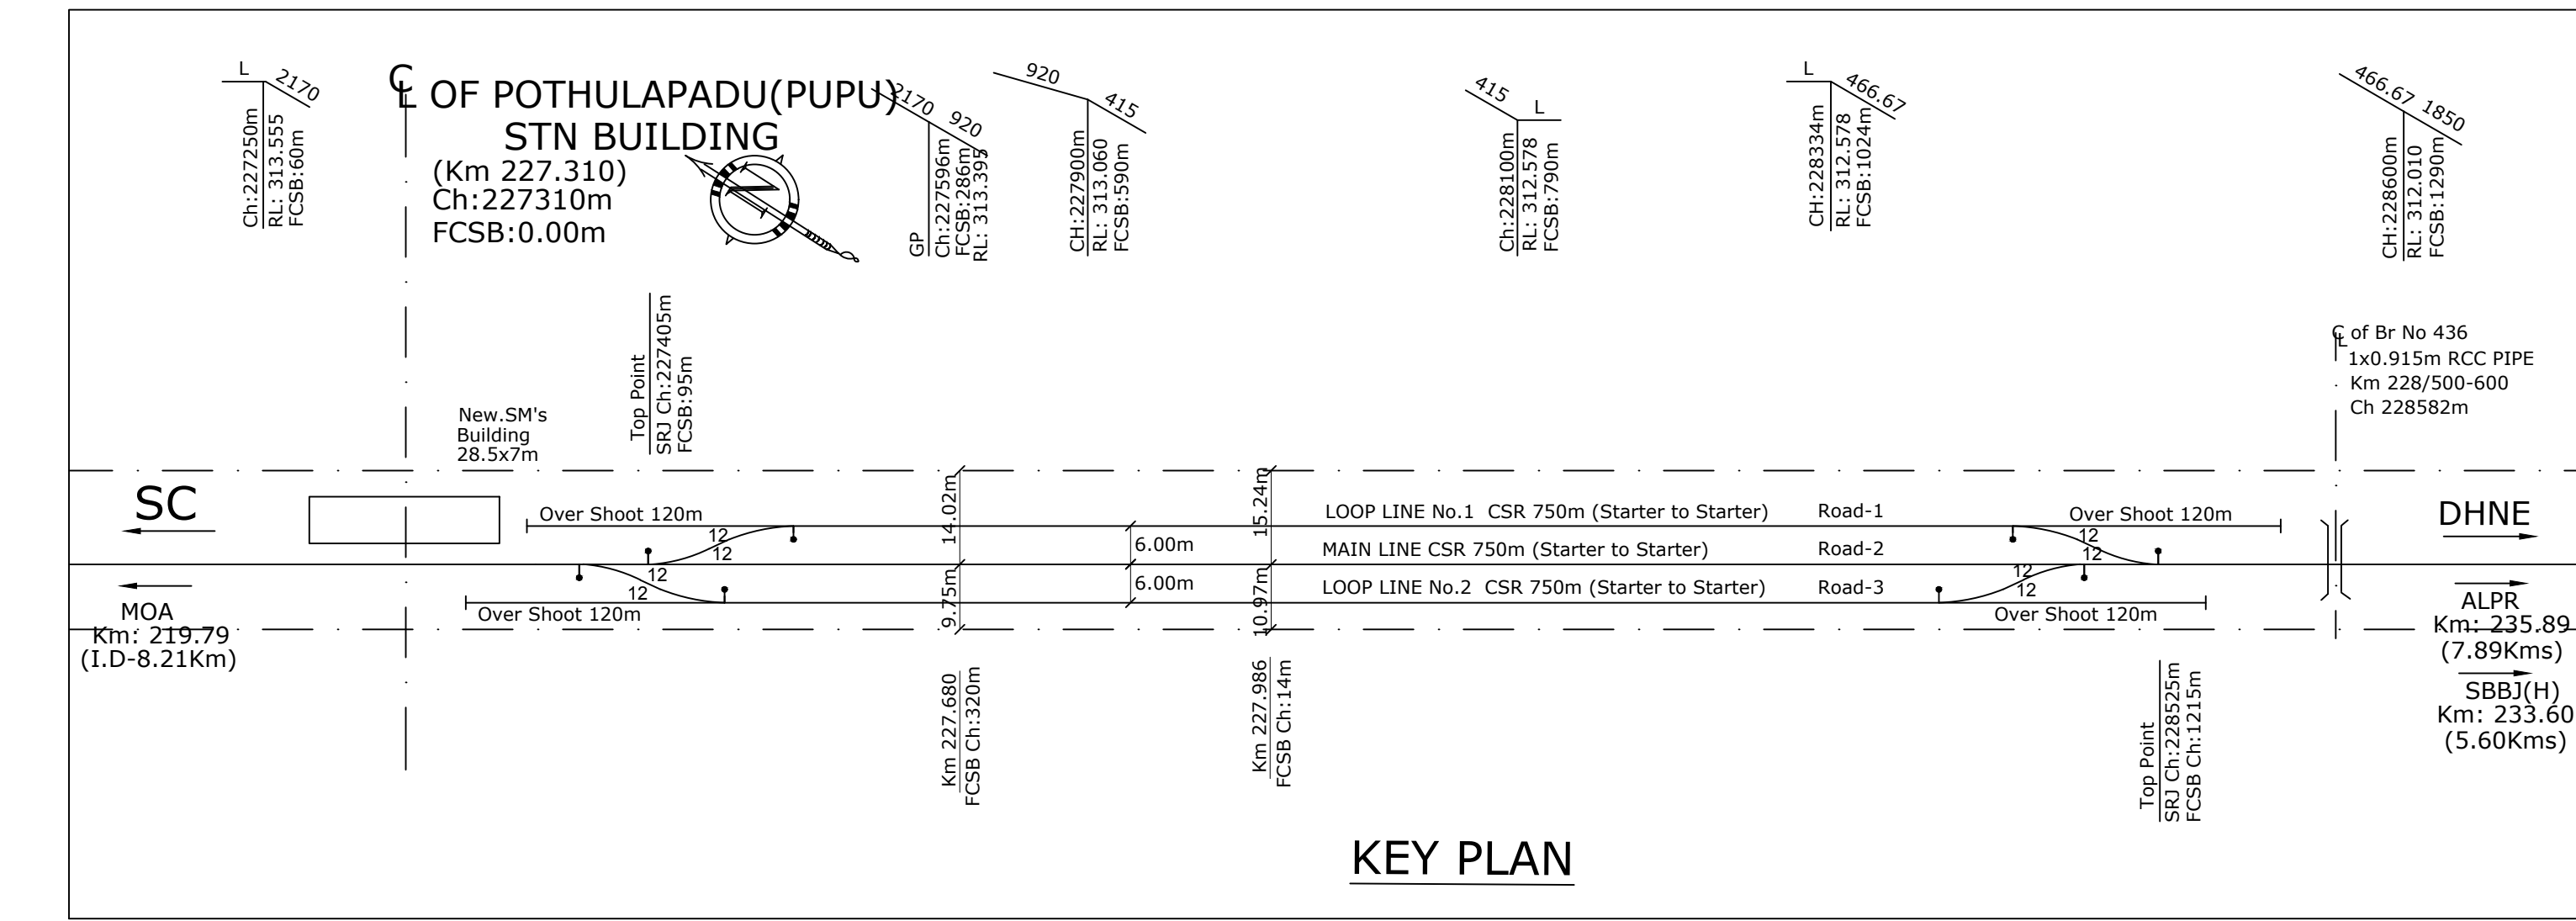


KEY PLAN

LIST OF PSRs AS PER WTT-79

- - - Nil - - -

GRADE INFRINGEMENTS IN THE YARD

- - - Nil - - -

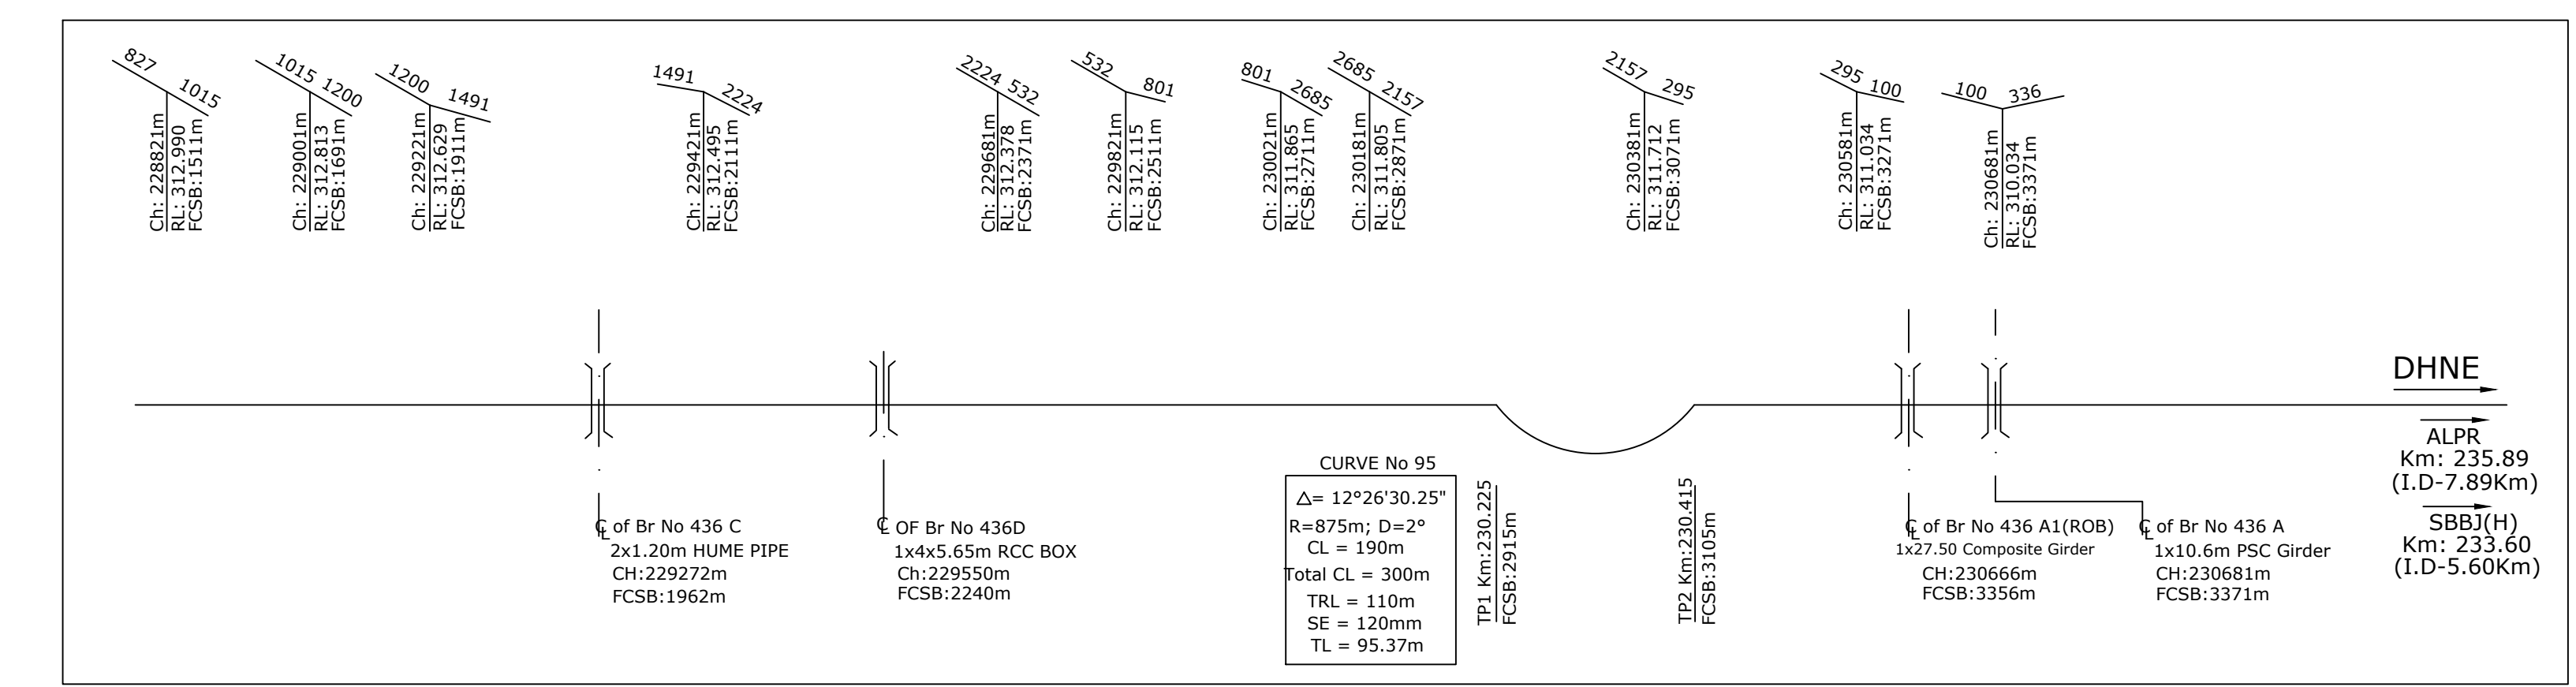

3 Km DETAILS ON DHNE END

- N O T E :
- THIS ESP IS PREPARED BASED ON THE EARLIER ESP APPROVED No. GW(W)SCYARDS/HYB/PUPU/619/2025 AND AS PER THE ACTUALS AT SITE.
 - LAND BOUNDARIES INDICATED IN THE DRAWING MAY NOT REFLECT THE ACTUAL RAILWAY BOUNDARY AND FOR RECKONING ACTUAL RAILWAY LAND, THE CERTIFIED LAND PLANS AS AVAILABLE AT HQ OR DIVISIONAL OFFICES IS FINAL AUTHORITY.

CERTIFIED THAT THE WORKS ARE CARRIED OUT AND EXECUTED AS PER THIS DRAWING	
SIGNATURE BLOCK	
DRM/HYB	
Sr.DEE/TR/HYB	
Sr.DSTE/HYB	
Sr.DOM/HYB	
Sr.DEN/Co-ORD-HYB	DURGA PRASAD P. T. V Digitally Signed by DURGA PRASAD P. T. V Date: 2025.08.18 14:38:29 +05'30'
DEN-LINES-HYB	ARUN KUMAR SHARMA Digitally Signed by ARUN KUMAR SHARMA Date: 2025.08.13 15:20:40 +05'30'

SOUTH CENTRAL RAILWAY		
Hqrs. Drg. No.	GM(W)SCYARDS/HYB/PUPU/COMP/65/2025	
Division Drg. No.	DRM (W) HYB / R-65 /2025	
Division	HYDERABAD	Section SC-DHNE
Station Name	POTHULAPADU	
Name of work	COMPLETION PLAN OF POTHULAPADU YARD: NEW CROSSING STATION BETWEEN MANOPAD AND ALAMPUR ROAD STATION.	
AUTHORITY	IRPSM ID: 11.03.16.17.1.52.001 (PB 89/17-18)	
SCALE	1Cm = 10M	